


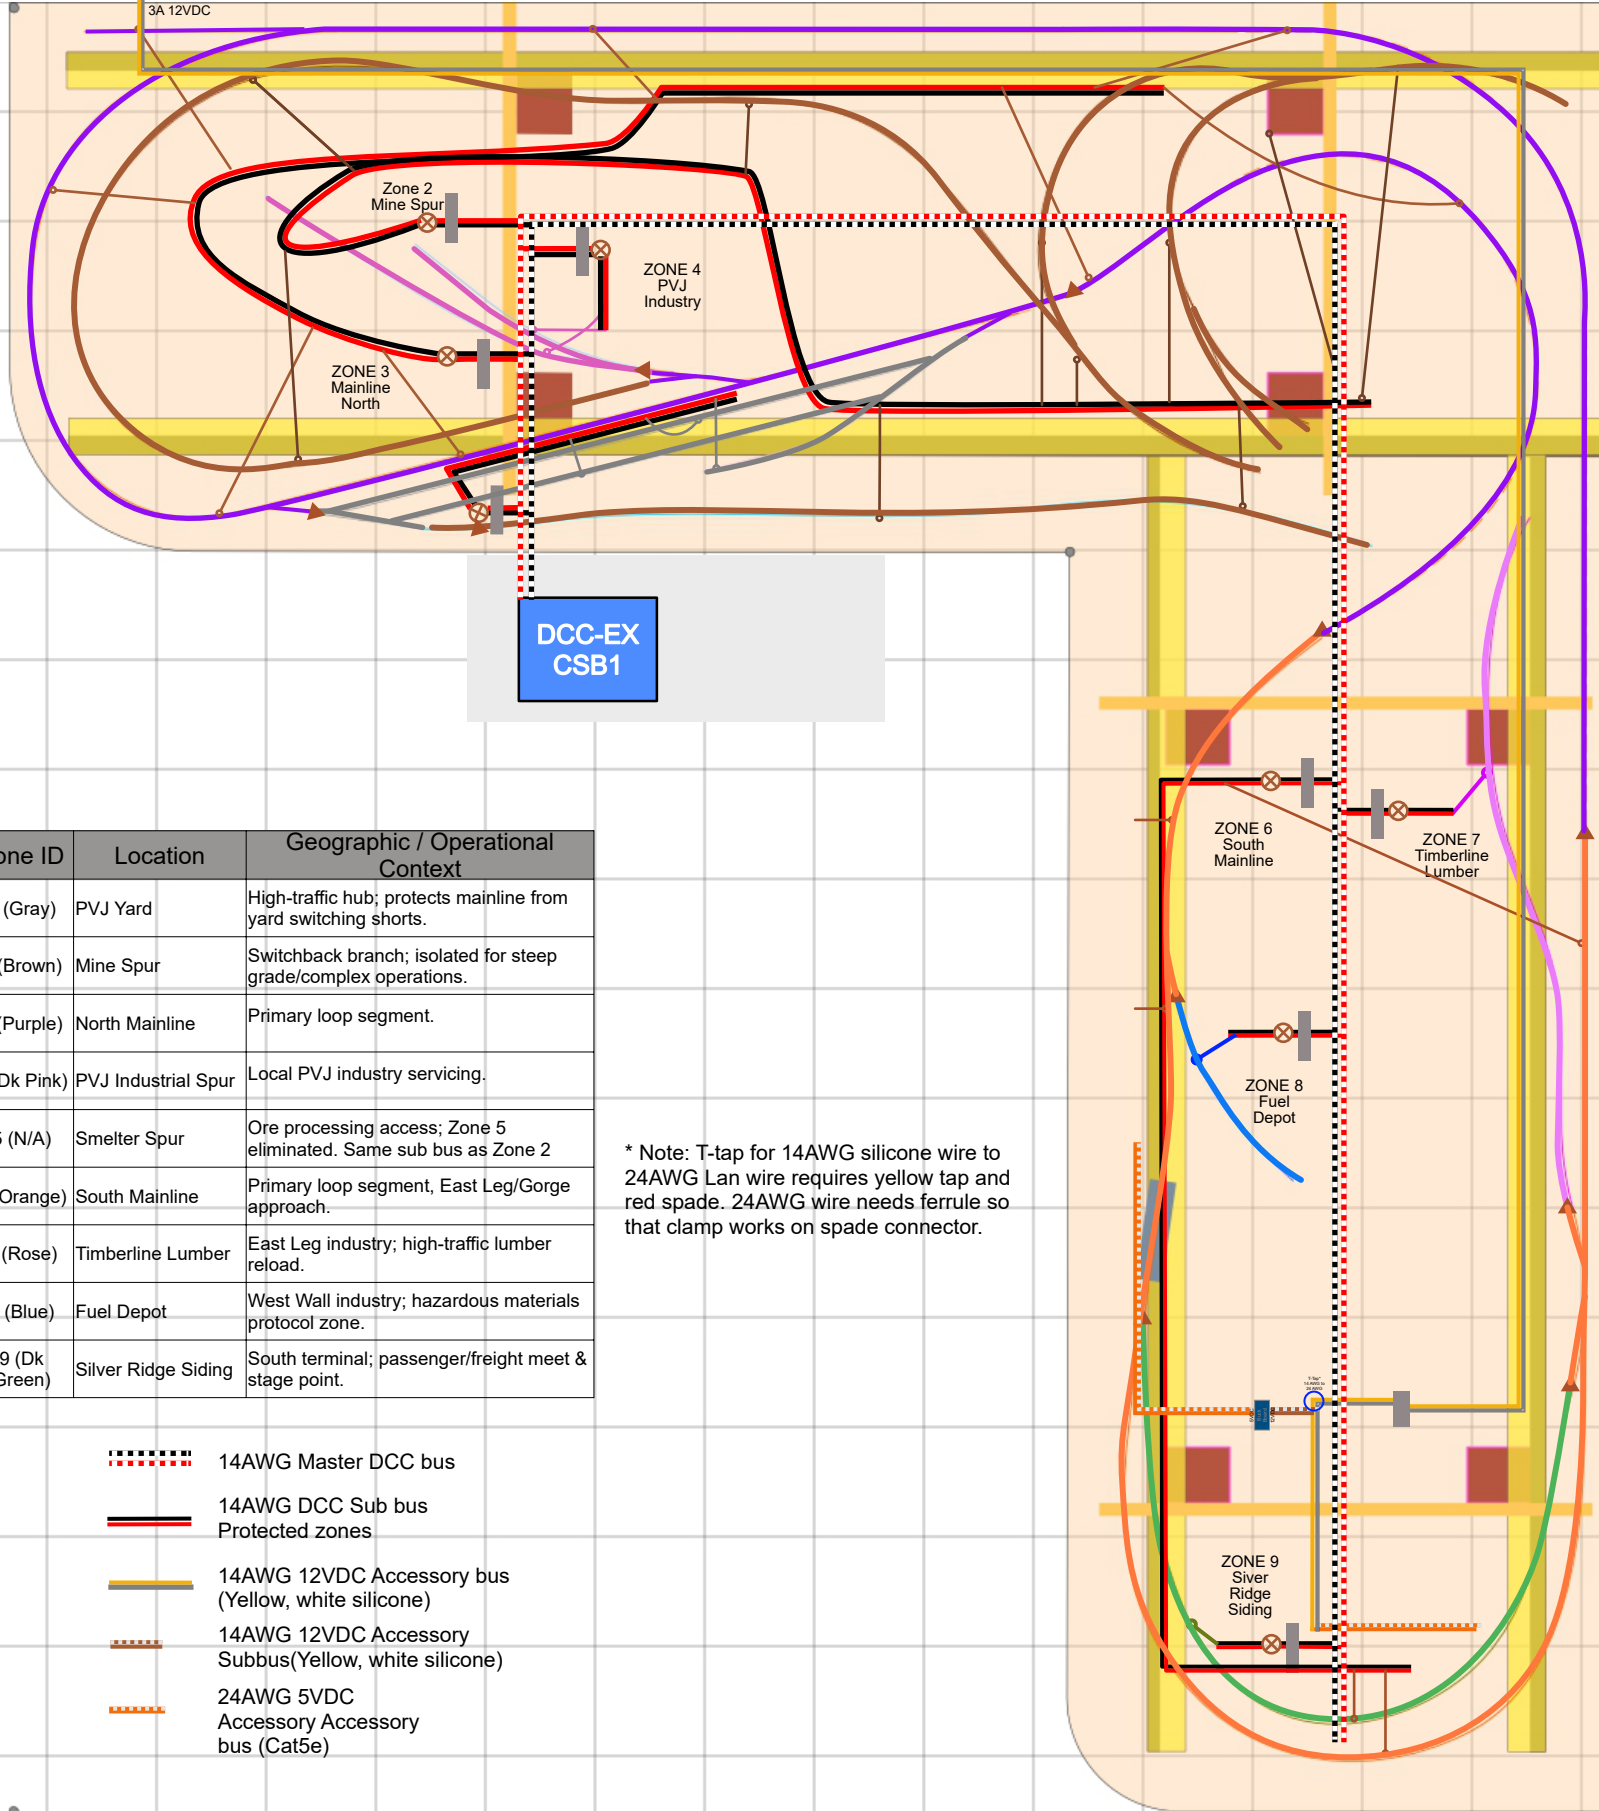

Zone ID	Location	Geographic / Operational Context
1 (Gray)	PVJ Yard	High-traffic hub; protects mainline from yard switching shorts.
2 (Brown)	Mine Spur	Switchback branch; isolated for steep grade/complex operations.
3 (Purple)	North Mainline	Primary loop segment.
4 (Dk Pink)	PVJ Industrial Spur	Local PVJ industry servicing.
5 (N/A)	Smelter Spur	Ore processing access; Zone 5 eliminated. Same sub bus as Zone 2
6 (Orange)	South Mainline	Primary loop segment, East Leg/Gorge approach.
7 (Rose)	Timberline Lumber	East Leg industry; high-traffic lumber reload.
8 (Blue)	Fuel Depot	West Wall industry; hazardous materials protocol zone.
9 (Dk Green)	Silver Ridge Siding	South terminal; passenger/freight meet & stage point.

* Note: T-tap for 14AWG silicone wire to 24AWG Lan wire requires yellow tap and red spade. 24AWG wire needs ferrule so that clamp works on spade connector.

- 14AWG Master DCC bus
- 14AWG DCC Sub bus
- Protected zones
- 14AWG 12VDC Accessory bus (Yellow, white silicone)
- 14AWG 12VDC Accessory Subbus (Yellow, white silicone)
- 24AWG 5VDC Accessory Accessory bus (Cat5e)